


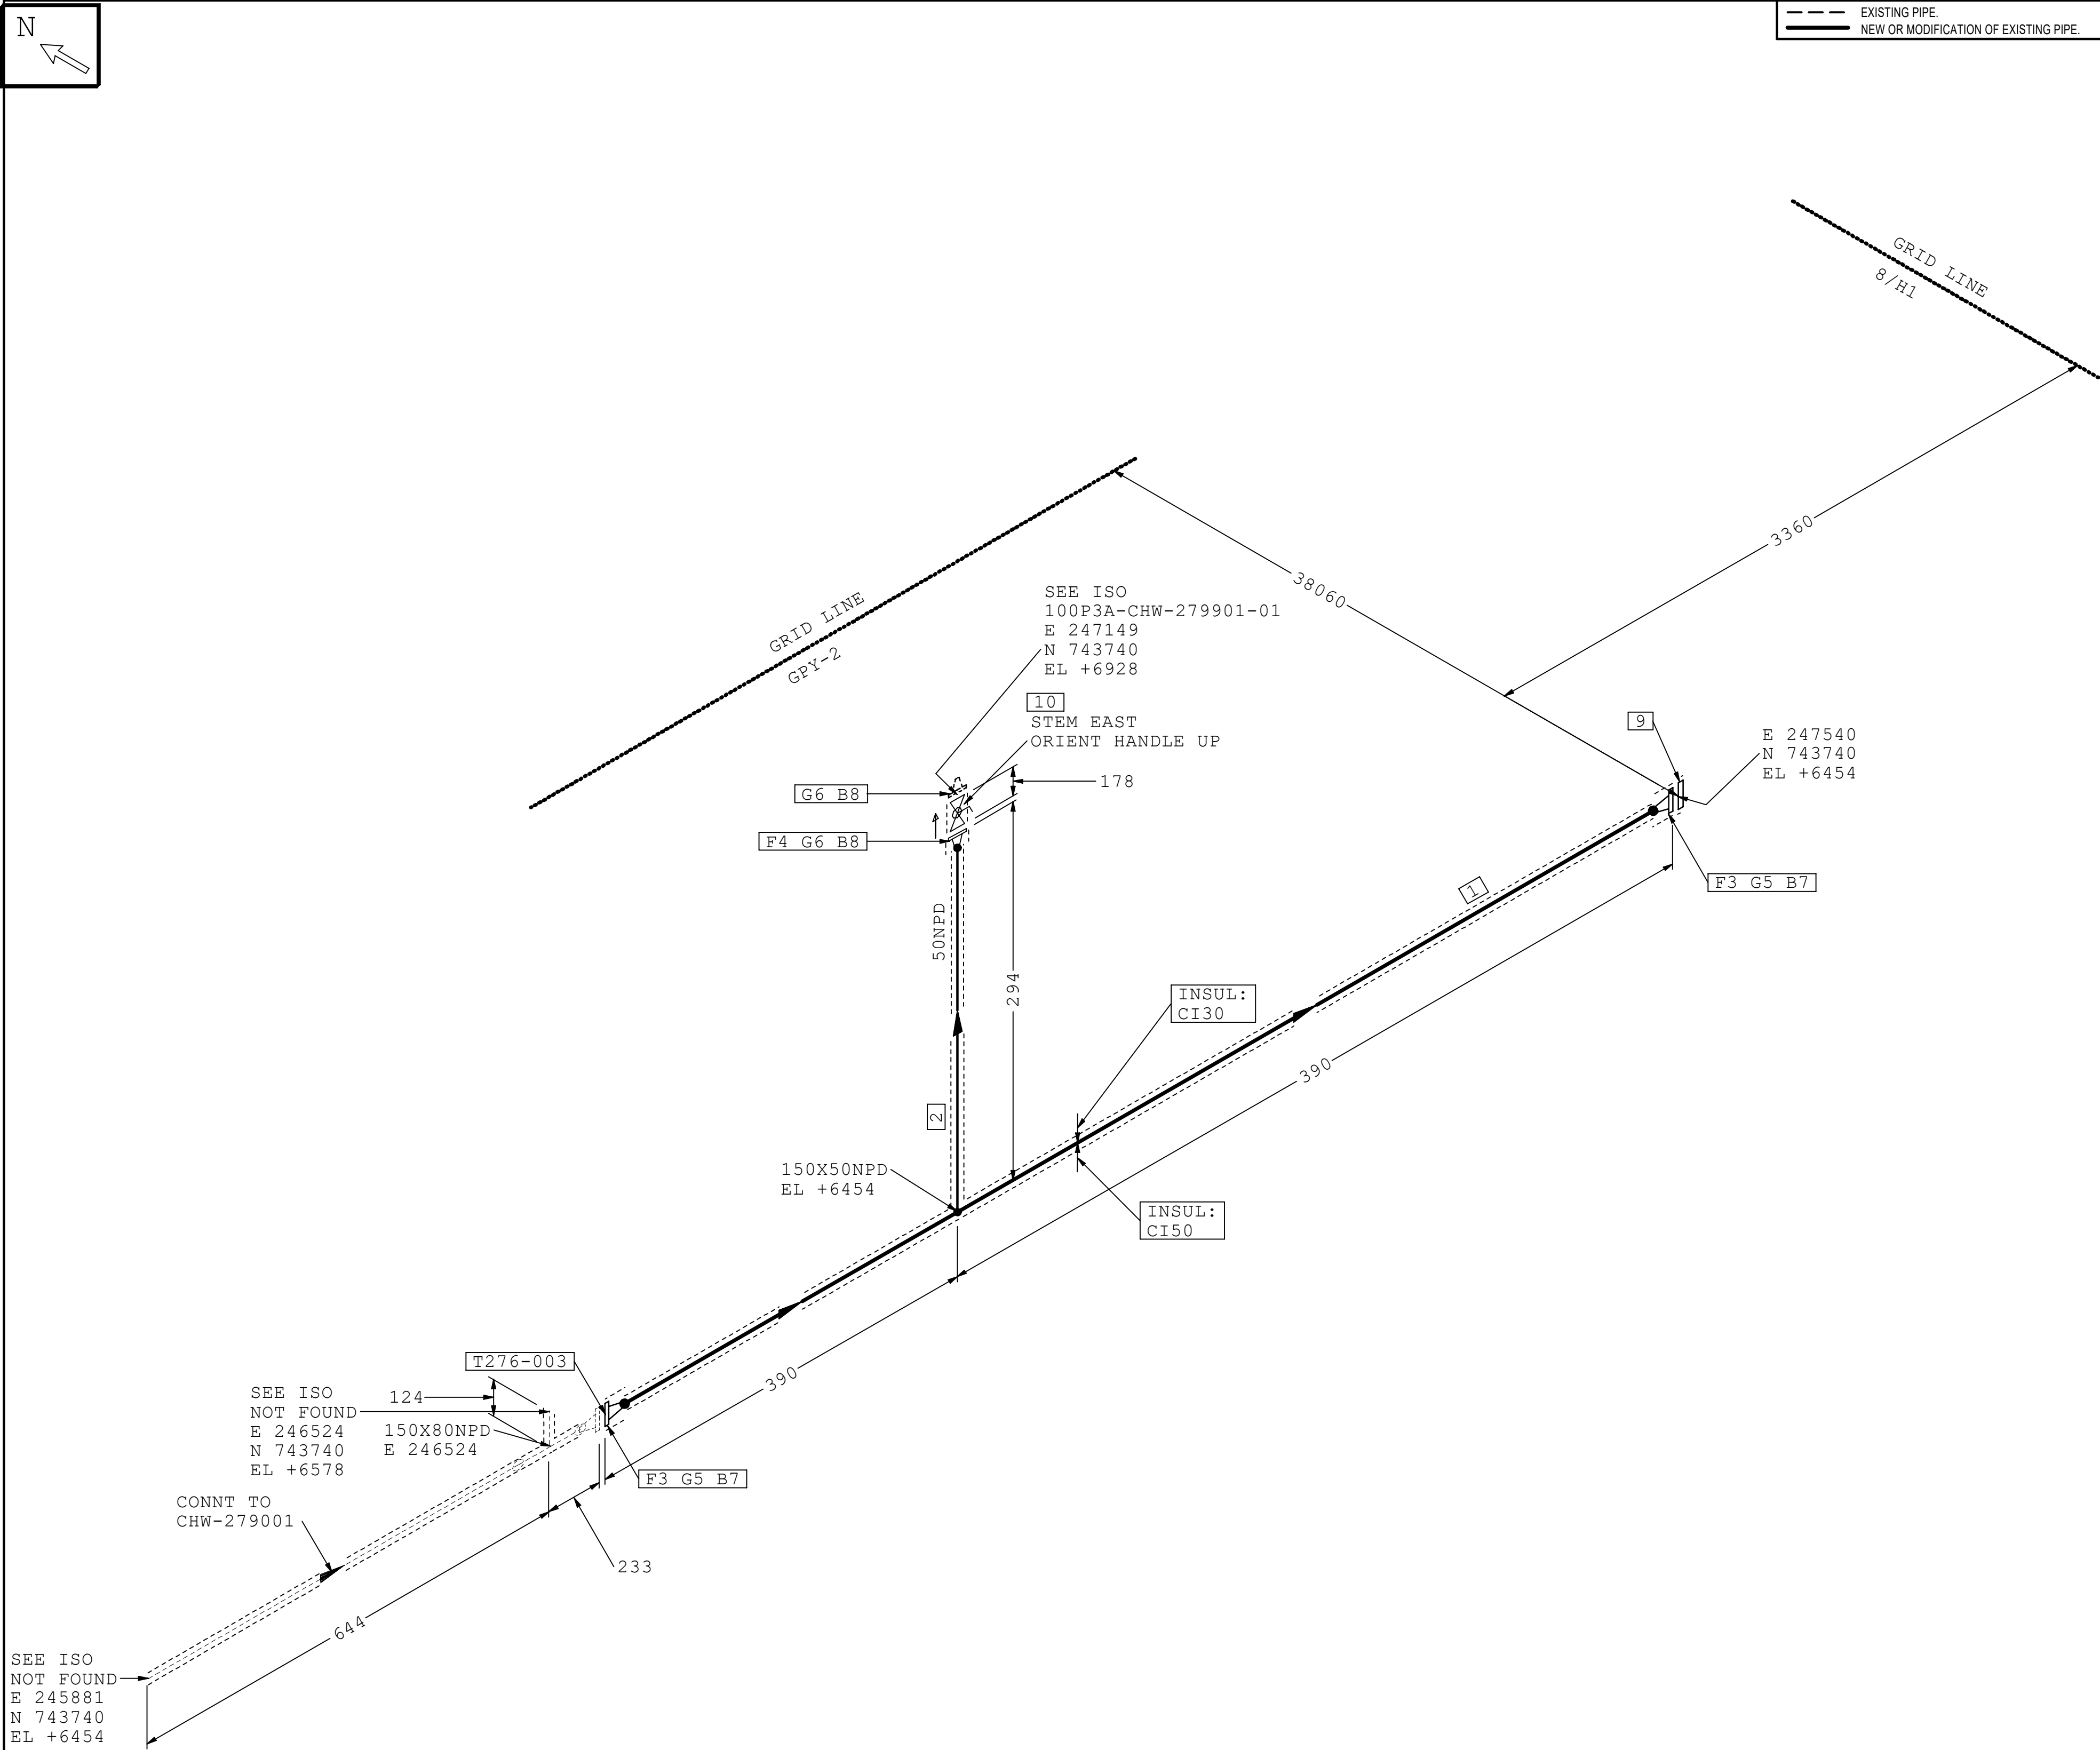

NOTES: 1. FOR HOLD ITEMS, TPT PIPING FIELD ENGINEER TO CONFIRM FINAL DIMENSION AT SITE.
2. PIPE ROUTING AND SUPPORTS OF LINES DN40 AND SMALLER (NO STRESS ANALYSED) ARE TO BE CONFIRMED AT SITE BY PIPING SUB-CONTRACTOR.
3. FOR STRESS ANALYSED LINES, NO CHANGES ALLOWED WITHOUT WRITTEN APPROVAL FROM PIPE STRESS ENGINEER.

EXTRACTION DATE: Today's Date (Locale Sensitive format) : 6/18/2026 9:01:37 AMToday's Date (Your format) : 18/06/26Today's Date (ISO8601 Small) : 2026-06-18 09:01:37

PT NO	MESC NO & COMPONENT DESCRIPTION	DIAM. (NS)	IDENT CODE	COMMODITY CODE	QTY
1	Pipes (Length),ASME B36.10,ASTM A106 Gr.B,BE,Seamless,, S-40, Undefined	150	CPP01J85	PPPP20C40230000000	0. 6 M
2	Pipes (Length),ASME B36.10,ASTM A106 Gr.B,BE,Seamless,, S-40, Undefined	50	CPPK&JJJ	PPPP20C40230000000	0. 2 M
3	WN Fig,ASME B16.5,ASTM A105,RF/BW End,150 Lbs., Undefined, S-40	150	CFGDKGPN	FGWN25C5C206L10000	2
4	WN Fig,ASME B16.5,ASTM A105,RF/BW End,150 Lbs., Undefined, S-40	50	C40A7VT	FGWN25C5C206L10000	1
PT NO	MESC NO & COMPONENT DESCRIPTION	DIAM. (NS)	IDENT CODE	COMMODITY CODE	QTY
5	NM Flat Gk,ASME B16.21,RF as per ASME B16.5,-,150 Lbs,	150	CZECARK	GKFG20900O0OL1000200	2
6	NM Flat Gk,ASME B16.21,RF as per ASME B16.5,-,150 Lbs,	50	CZECARD	GKFG20900O0OL1000200	2
7	SBlt 2 HHx N,ASME B18.2.1/ASME B18.2.2,Full Length Threaded, - 110 mm Length	3/4	C111DH8Z	BTS222A005010D00	16
8	SBlt 2 HHx N,ASME B18.2.1/ASME B18.2.2,Full Length Threaded, - 90 mm Length	5/8	C111DH8X	BTS222A005010D00	8
VALVES / IN-LINE ITEMS					
9	Bld Fig,ASME B16.5,ASTM A105,RF,150 Lbs., Undefined, Undefined	150	CFGDKG5S	FGBL25C5C202L10000	1
10	Bal Fig,RB,L.P,ISO 17292,ASTM A216 Gr,WCB,RF,150 Lbs., Undefined, Undefined	50	CVRN9YV	VBAG80C4000AL1KZ070L00	1

1	2026.06.22	UPDATE FOR CONSTRUCTION	ZMF	ZLF	
0	2026.04.03	ISSUE FOR CONSTRUCTION	ZMF	ZLF	
REV	DATE	DESCRIPTION	DRAWN	CHECKED	APPROVED

BANC PANDA3 PROJECT 蓝星安迪苏南京液体蛋氨酸装置技术改造项目					
		T.EN Chemical Engineering (Tianjin) Co.,LTD 德希尼布化学工程（天津）有限公司		 Bluestar Adisseo Nanjing Co.,LTD 蓝星安迪苏南京有限公司	
PIPING ISOMETRIC					
UNIT	AREA		INSU. THK	STRESS CAT	DOCUMENT CLASS
270	100P3A		50 mm		B
LINE NUMBER					MARIAN SHEET
150 CHW 279001 A1AA07 CI					01
PID NO.				SHEET	REV
2069N-270-PID-0031-279				1 OF 1	1

TPC S3D_BANC2\BANC1\100\2069N\Piping\Pipelines-Tie-In\2069N-270-PID-0031-279

100P3A-CHW-279001-01

100P3A-CHW-279001-01